

La thème de ce document est une concept original de DEF et sa propriété exclusive. Toute reproduction non autorisée serait possible de poursuite.

© DEF

Rédacteur	A. VEZIEN
Approbateur	
C	AJOUT DES PLANS NIVEAUX R+1 et R+2
Indice	Date

Modifications

PLAN DE ZONES DETECTION INCENDIE

R+1

AFFAIRE 1 APST - FOYER LES TAMARIS

DEF

IDF SUD & EST - ALLEE DES VOYAGEURS


BULEVARD DE COURRIN

77165 LIGNES - TEL. 016951450

No d'affaire 0330401

Plan iP2001

Folio 13/5

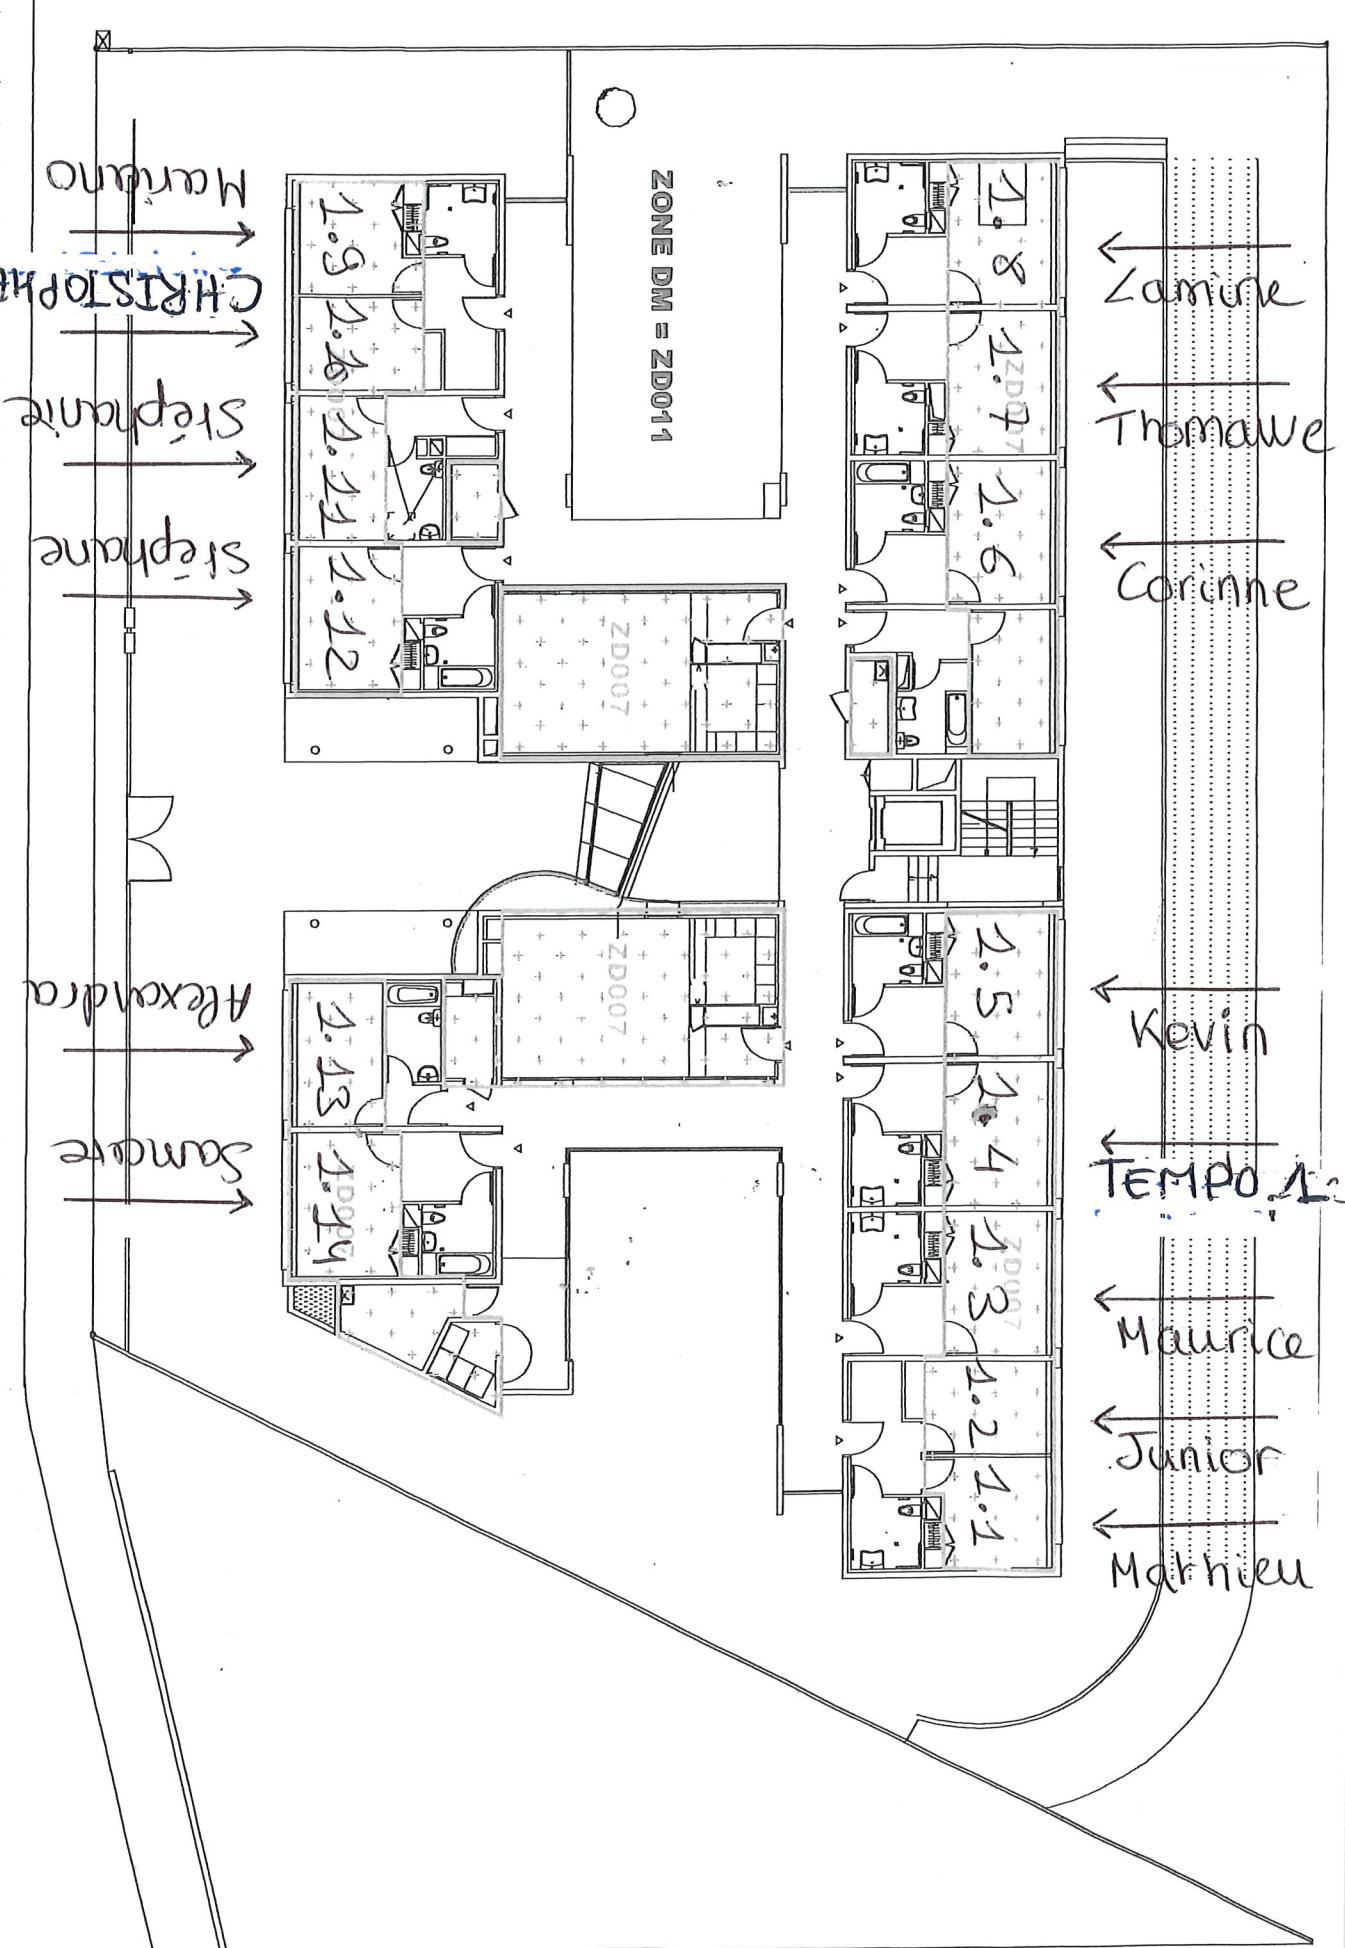

La traçage de ce document est une conception originale

DEF

et sa propriété exclusive. Toute reproduction non autorisée serait passible de poursuite.

Rédacteur

A. VEZIEN

Approbateur

A. CHOSROVA




C	03/04/09	AJOUT DES PLANS NIVEAUX R+1 et R+2
Indice	Date	Modifications

PLAN DE ZONES DETECTION INCENDIE R+2


AFFAIRE 1

APIST - FOYER LES TAMARIS

IUF SUD & EST - ALLEE DES VOYAGEURS
77165 LOGNES - TEL. 0160.951450

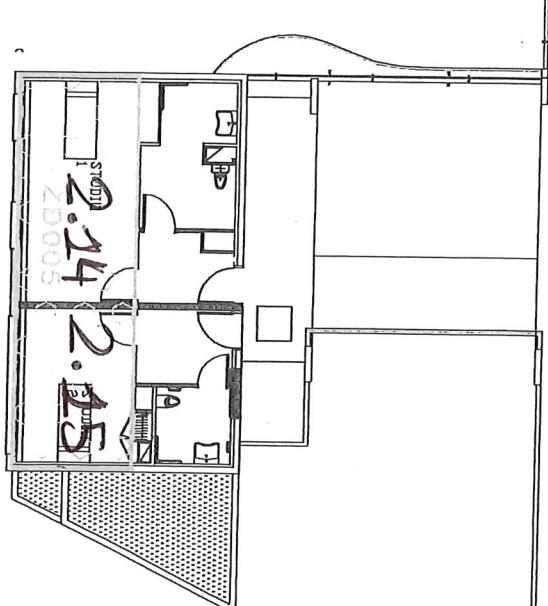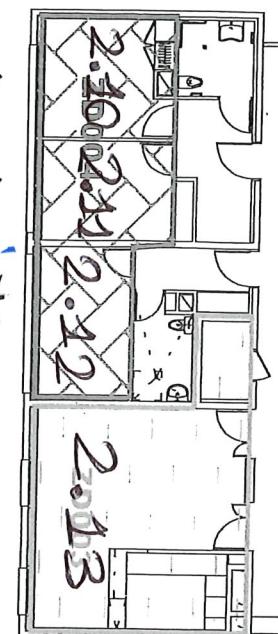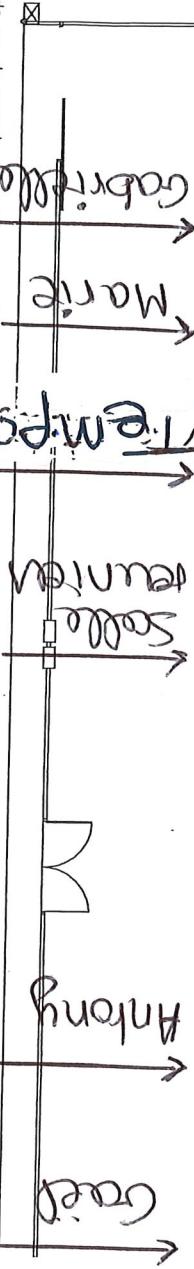

ZONE DM = ZD012

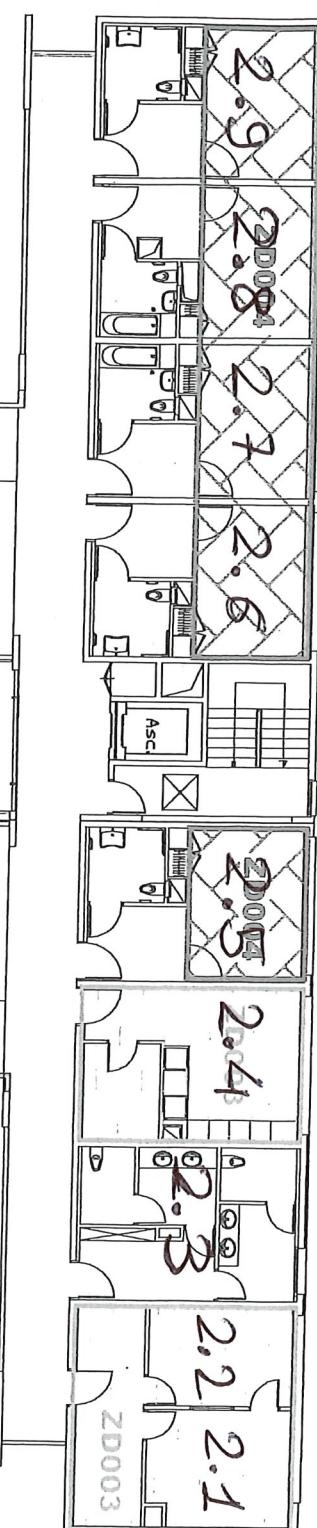

- ← Faouzi
- ← Tayeb
- ← Erwan
- ← Federico
- ← Margerie
- ← Laverie
- ← Salle esthétique
- ← Salle de pause
- ← Salle de pause

La traçage de ce document est une conception originale

DEF

et sa propriété exclusive. Toute reproduction non autorisée serait passible de poursuite.